

TAŞKIŞLA

ITU FACULTY OF ARCHITECTURE / 1850–2026 / 132 × 95 m

Historical plan vs. contemporary function — a walkability inquiry

N ^

POSTER 01 / 02 — THE BUILDING
181 SPACES · 20 LIFTED
ŞEYMA OLCAY

· 07 Jun 2026 ·

Top 20 spaces by walkability: priority-weighted inverse step depth from main entrance.

20 / 181

spaces lifted

11% high walkability

18

on ground floor

closest to entrance

1

on 1st floor

2–3 steps from entry

0

on 2nd floor

far from entrance

1


in basement

deepest, isolated

RESEARCH QUESTION

Does Taşkişla's 1850 plan, designed as military barracks, align with the walkability needs of today's architectural education?

VISUAL GRAMMAR

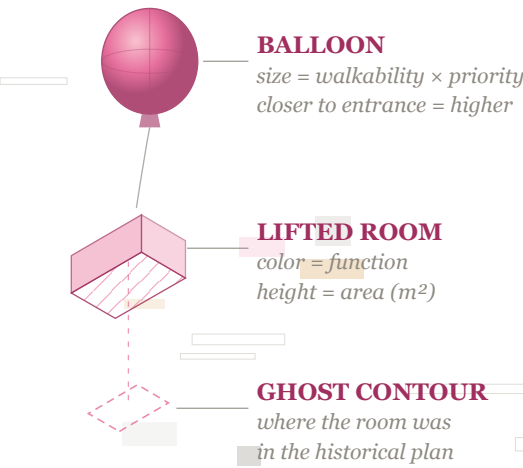

The building stands inverted — tradition turned upside down. Aligned spaces rise; function reverses gravity.

INTENDED AUDIENCE

- Architects & spatial designers
- Space syntax researchers
- Adaptive reuse specialists
- Heritage building consultants

METHODOLOGY

1. Plan reading > 181 spaces
2. Rhino + GH > geometry
3. Python + NetworkX > graph
4. Alignment scoring


walkability = 1 - step/max
alignment = walk × prio/5

KEY MESSAGE

The historical plan absorbs public, educational uses on the ground floor — but pushes production-heavy programs (workshops, labs) into deep, isolated positions that the 1850 barracks logic still imposes on the building.

FUNCTION TYPOLOGY

Lecture / Studio	61 · critical
Faculty room	35 · medium
Office	19 · medium
Workshop	14 · high
Administrative	13 · medium
Research centre	8 · medium
Archive	4 · peripheral
Laboratory	3 · high
Library	2 · critical
Circulation	10 · low
Exhibition	1 · critical
Conference	2 · critical
Meeting	2 · high
Institute	2 · medium
Virtual studio	1 · high
WC	2 · peripheral
Technical service	1 · peripheral

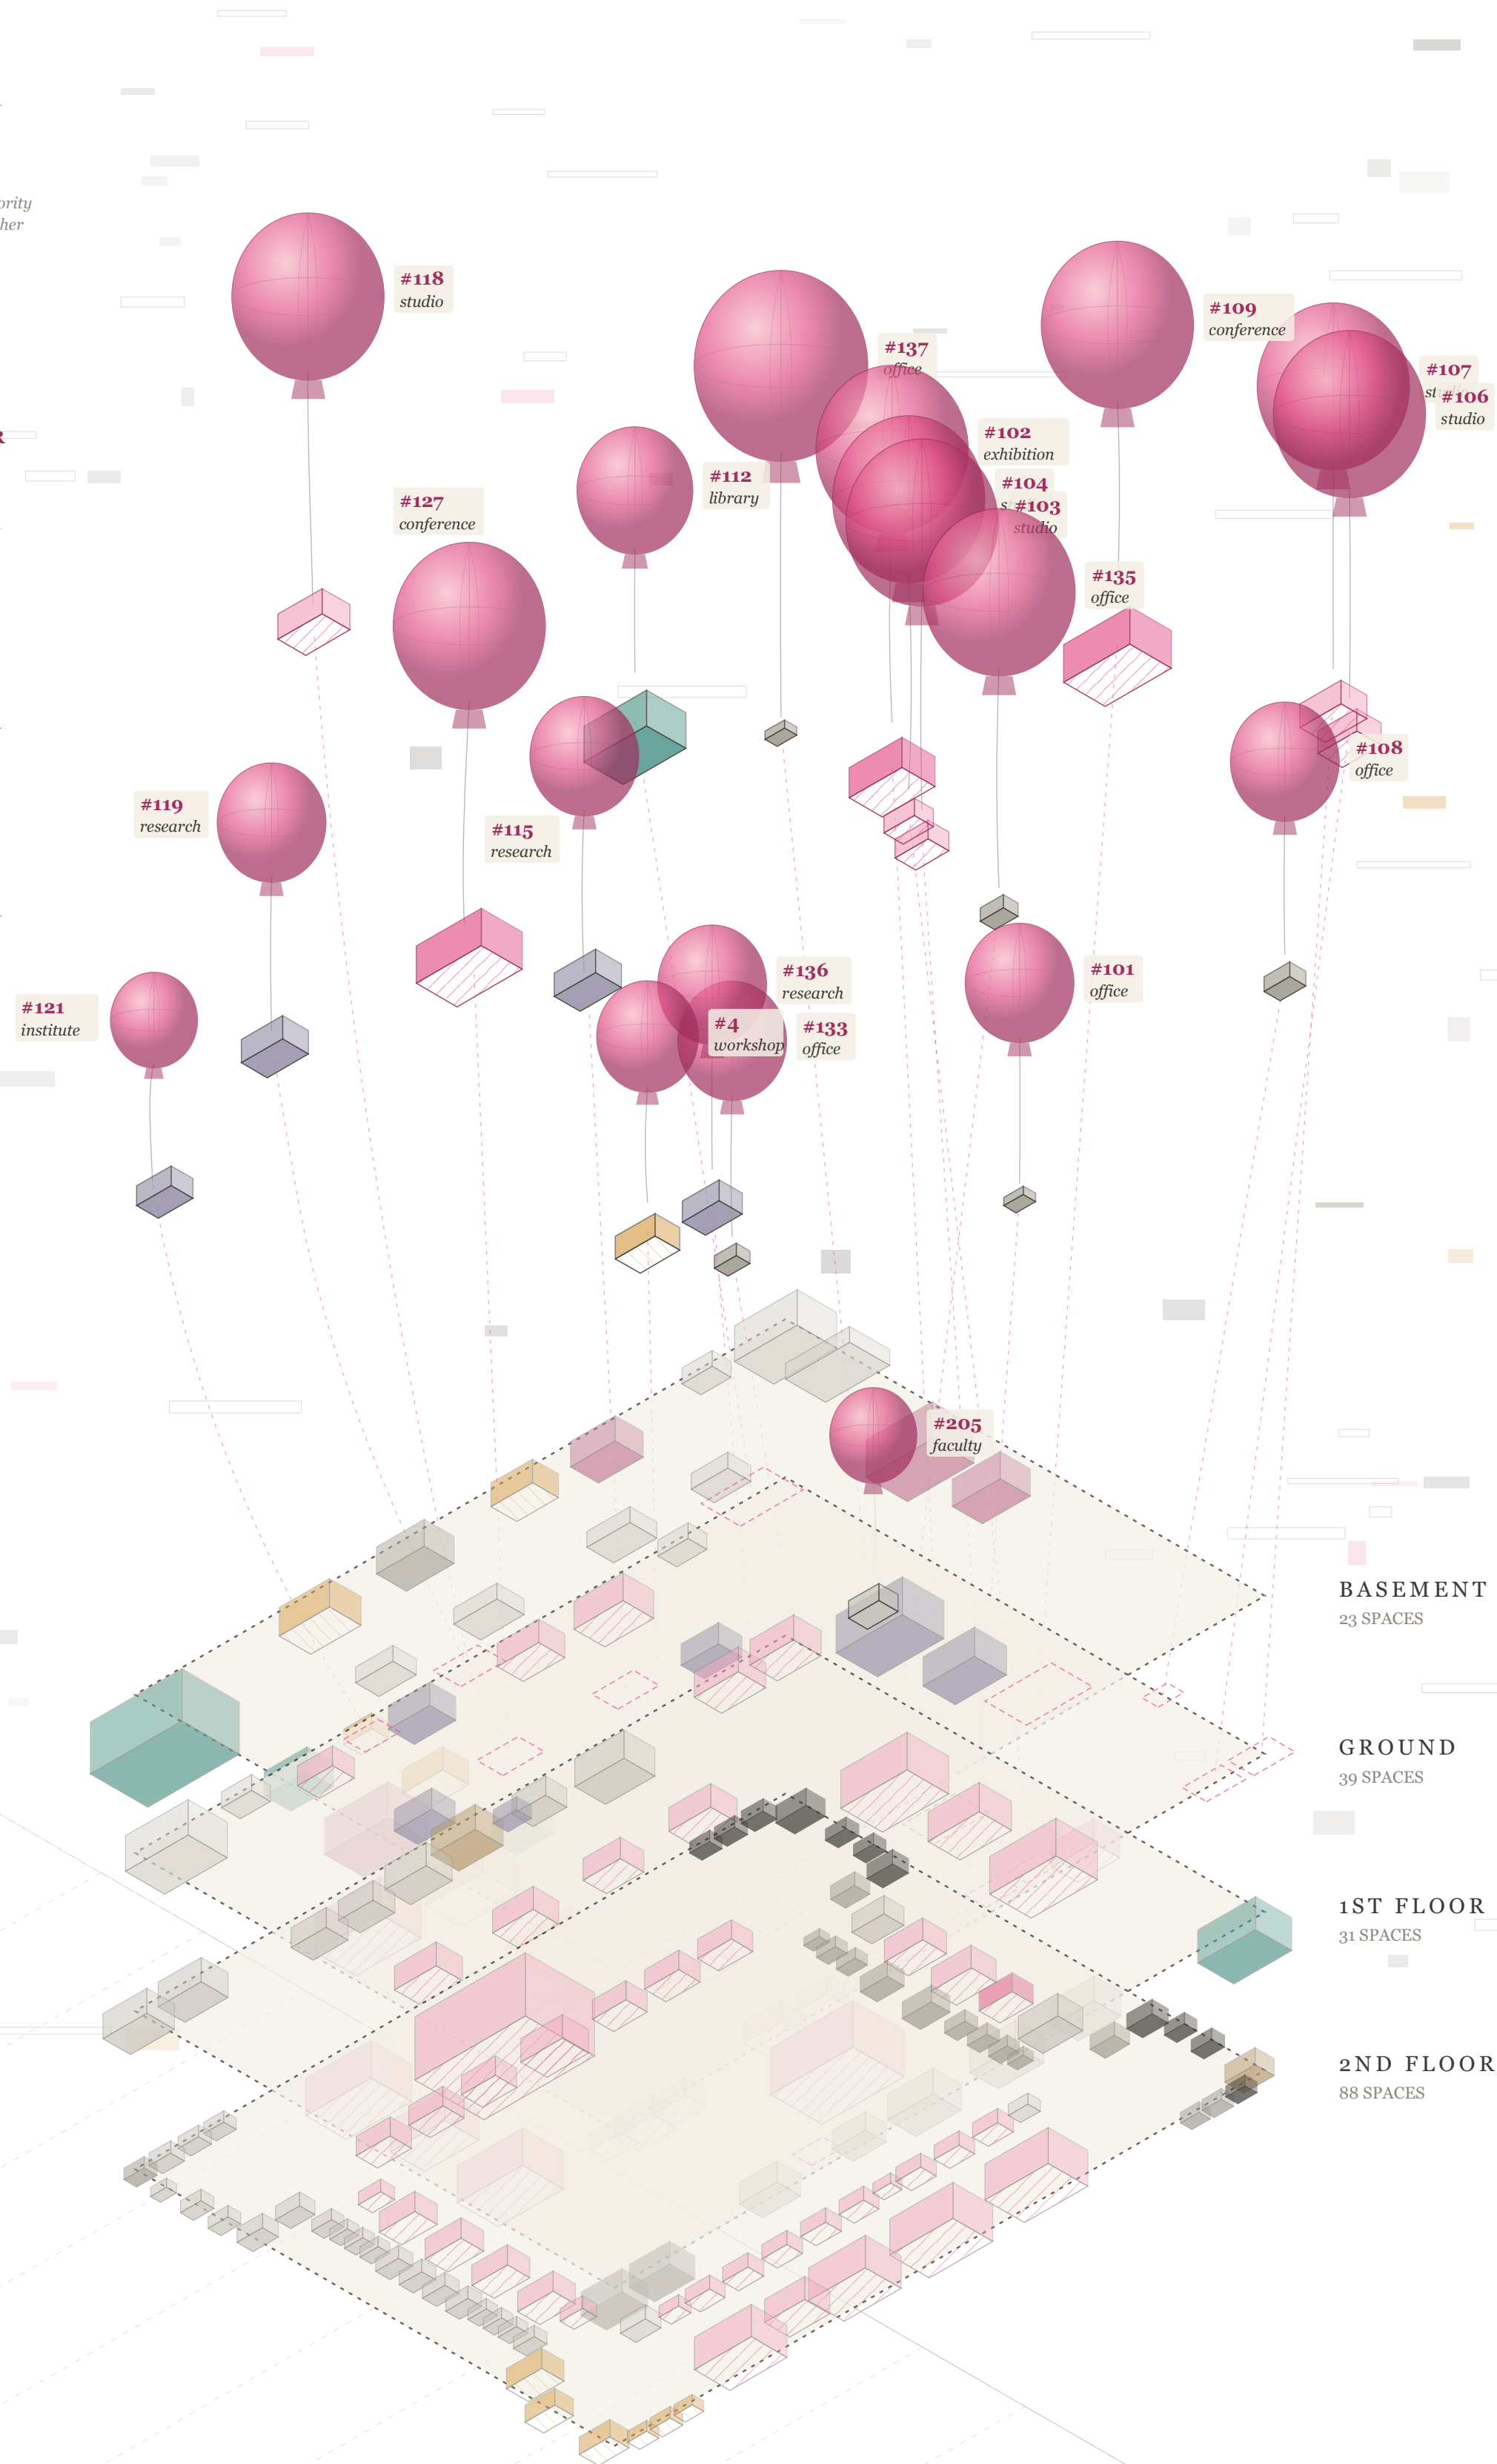

BASEMENT

23 SPACES

GROUND

39 SPACES

1ST FLOOR

31 SPACES

2ND FLOOR

88 SPACES